


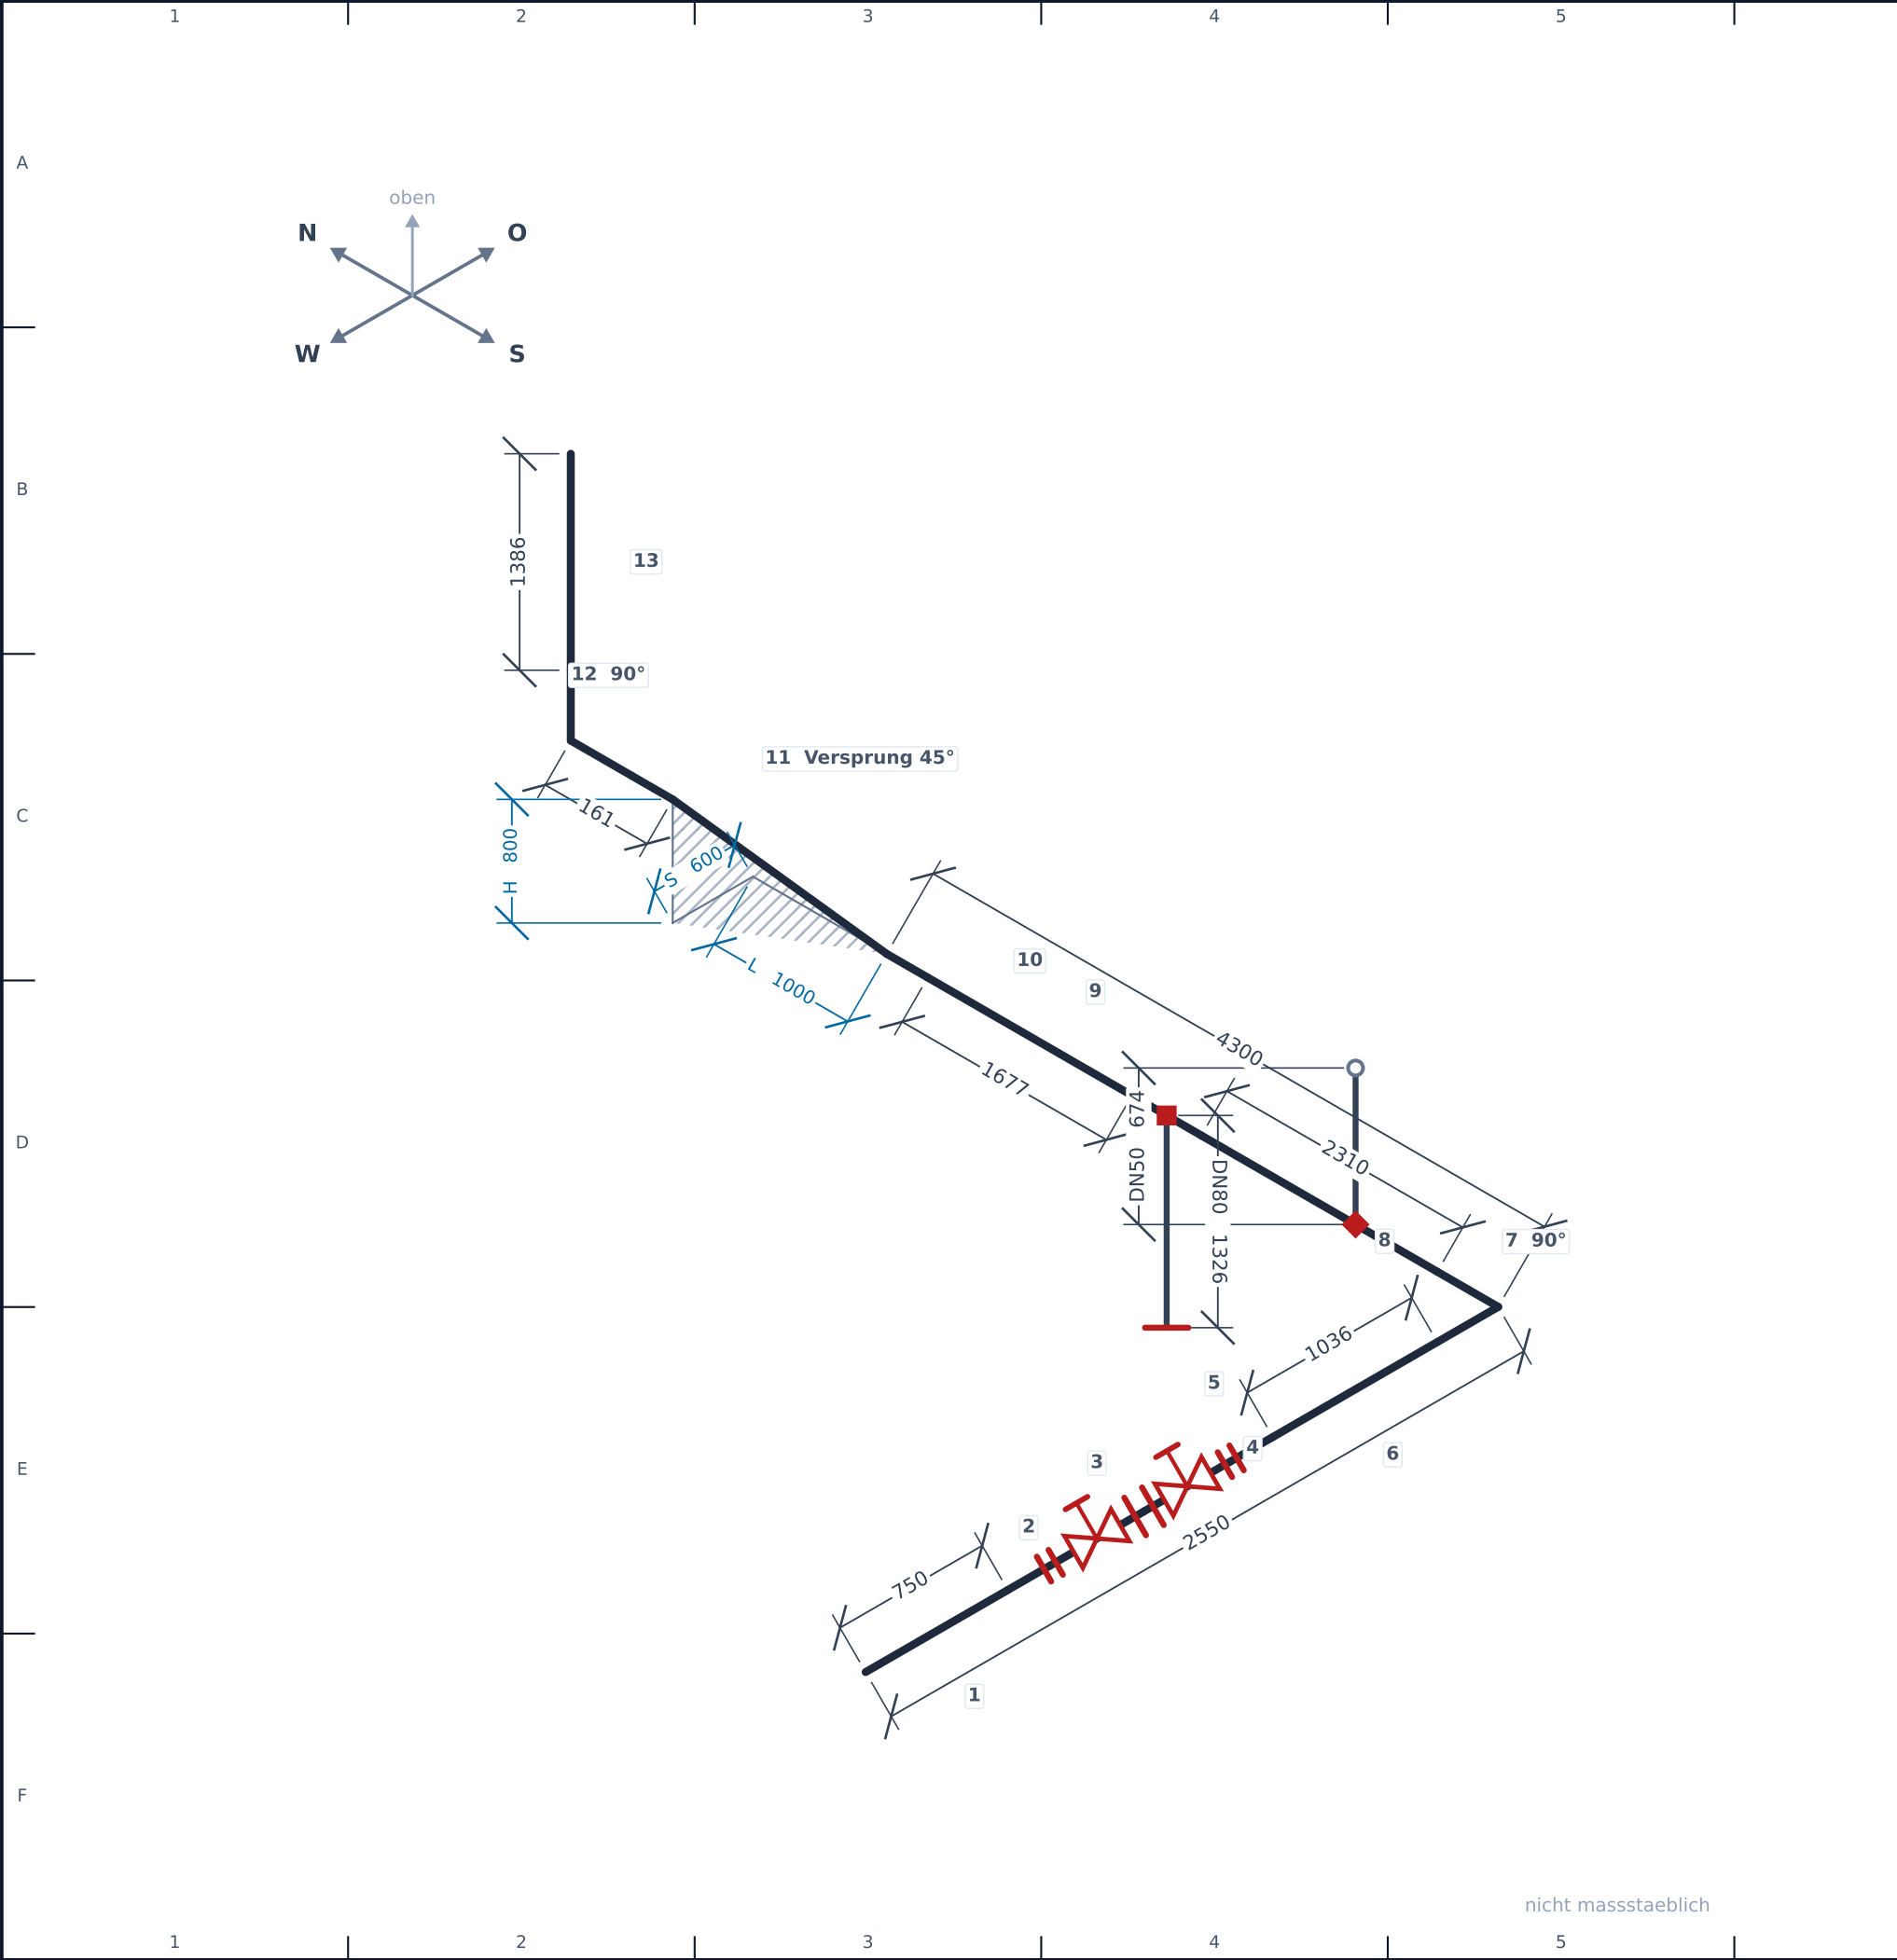

Stueckliste

Pos	Anzahl	Benennung	DN	Wand	Werkstoff	Norm
1	0.60 m	Rohr	50	3.91	P235GH	EN 10216-2
2	9.68 m	Rohr	80	5.49	P235GH	EN 10216-2
3	1 St	Anschweisstutzen	50	3.91	P235GH	MSS SP-97
4	2 St	Armatur mit Flanschen	80		P235GH	EN 558
5	2 St	Bogen 45 Grad	80	5.49	P235GH	EN 10253-2
6	2 St	Bogen 90	80	5.49	P235GH	EN 10253-2
7	1 St	T-Stueck	80	5.49	P235GH	EN 10253-2
8	1 St	T-Stueck (Abzweig)	80	5.49	P235GH	EN 10253-2

... 3 weitere Positionen - siehe Excel

Nahtliste

Naht	Art	DN	Ort	Wo
WF1	Rundnaht	80	Anschluss Anfang	Baustelle
WF2	Rundnaht	80	Rohr / Vorschweisflansch	Werkstatt
WF3	Flanschverbindung	80	Vorschweisflansch / Armatur mit Flanschen	Werkstatt
WF4	Flanschverbindung	80	Armatur mit Flanschen / Armatur mit Flansc...	Werkstatt
WF5	Flanschverbindung	80	Armatur mit Flanschen / Vorschweisflansch	Werkstatt
WF6	Rundnaht	80	Vorschweisflansch / Rohr	Werkstatt
WF7	Rundnaht	80	Rohr / Bogen 90	Werkstatt
WF8	Rundnaht	80	Bogen 90 / Rohr	Werkstatt
WF9	Rundnaht	50	Anschweisstutzen auf DN 80	Werkstatt
WF10	Rundnaht	50	Abzweigrohr angeschweisst	Werkstatt
WF11	Rundnaht	80	Rohr / T-Stueck	Werkstatt
WF12	Rundnaht	80	Fertig-T Durchgang 1	Werkstatt
WF13	Rundnaht	80	Fertig-T Durchgang 2	Werkstatt
WF14	Rundnaht	80	Abzweigrohr angeschweisst	Werkstatt
WF15	Rundnaht	80	Abzweig / Vorschweisflansch	Werkstatt
WF16	Flanschverbindung	80	Abzweig Flanschanschluss	Baustelle


... 7 weitere Naehnte - siehe Excel

Legende

- Werkstattnaht
- Baustellennaht
- Vorschweisflansch
- Armatur
- Fertig-T
- Anschweisstutzen
- Positionsnummer aus der Stueckliste

PipeCraft - Rohrfolge

Zeichnung ISO-1001	Leitung 80-PL-1001-P235GH
Projekt / Anlage Testanlage Nord	NPD DN 80
Werkstoff P235GH	Schedule STD
Auslegungsdruck 16 bar	Auslegungstemperatur 120 Grad C
Isolierung 60 mm MW	Rohr gesamt 11.93 m
Naehnte / Flansche 19 / 4	Baustellennaehnte 3
Erstellt von T. Brors	Datum / Ansicht 05.09.2026 · Aufmass & Saegen

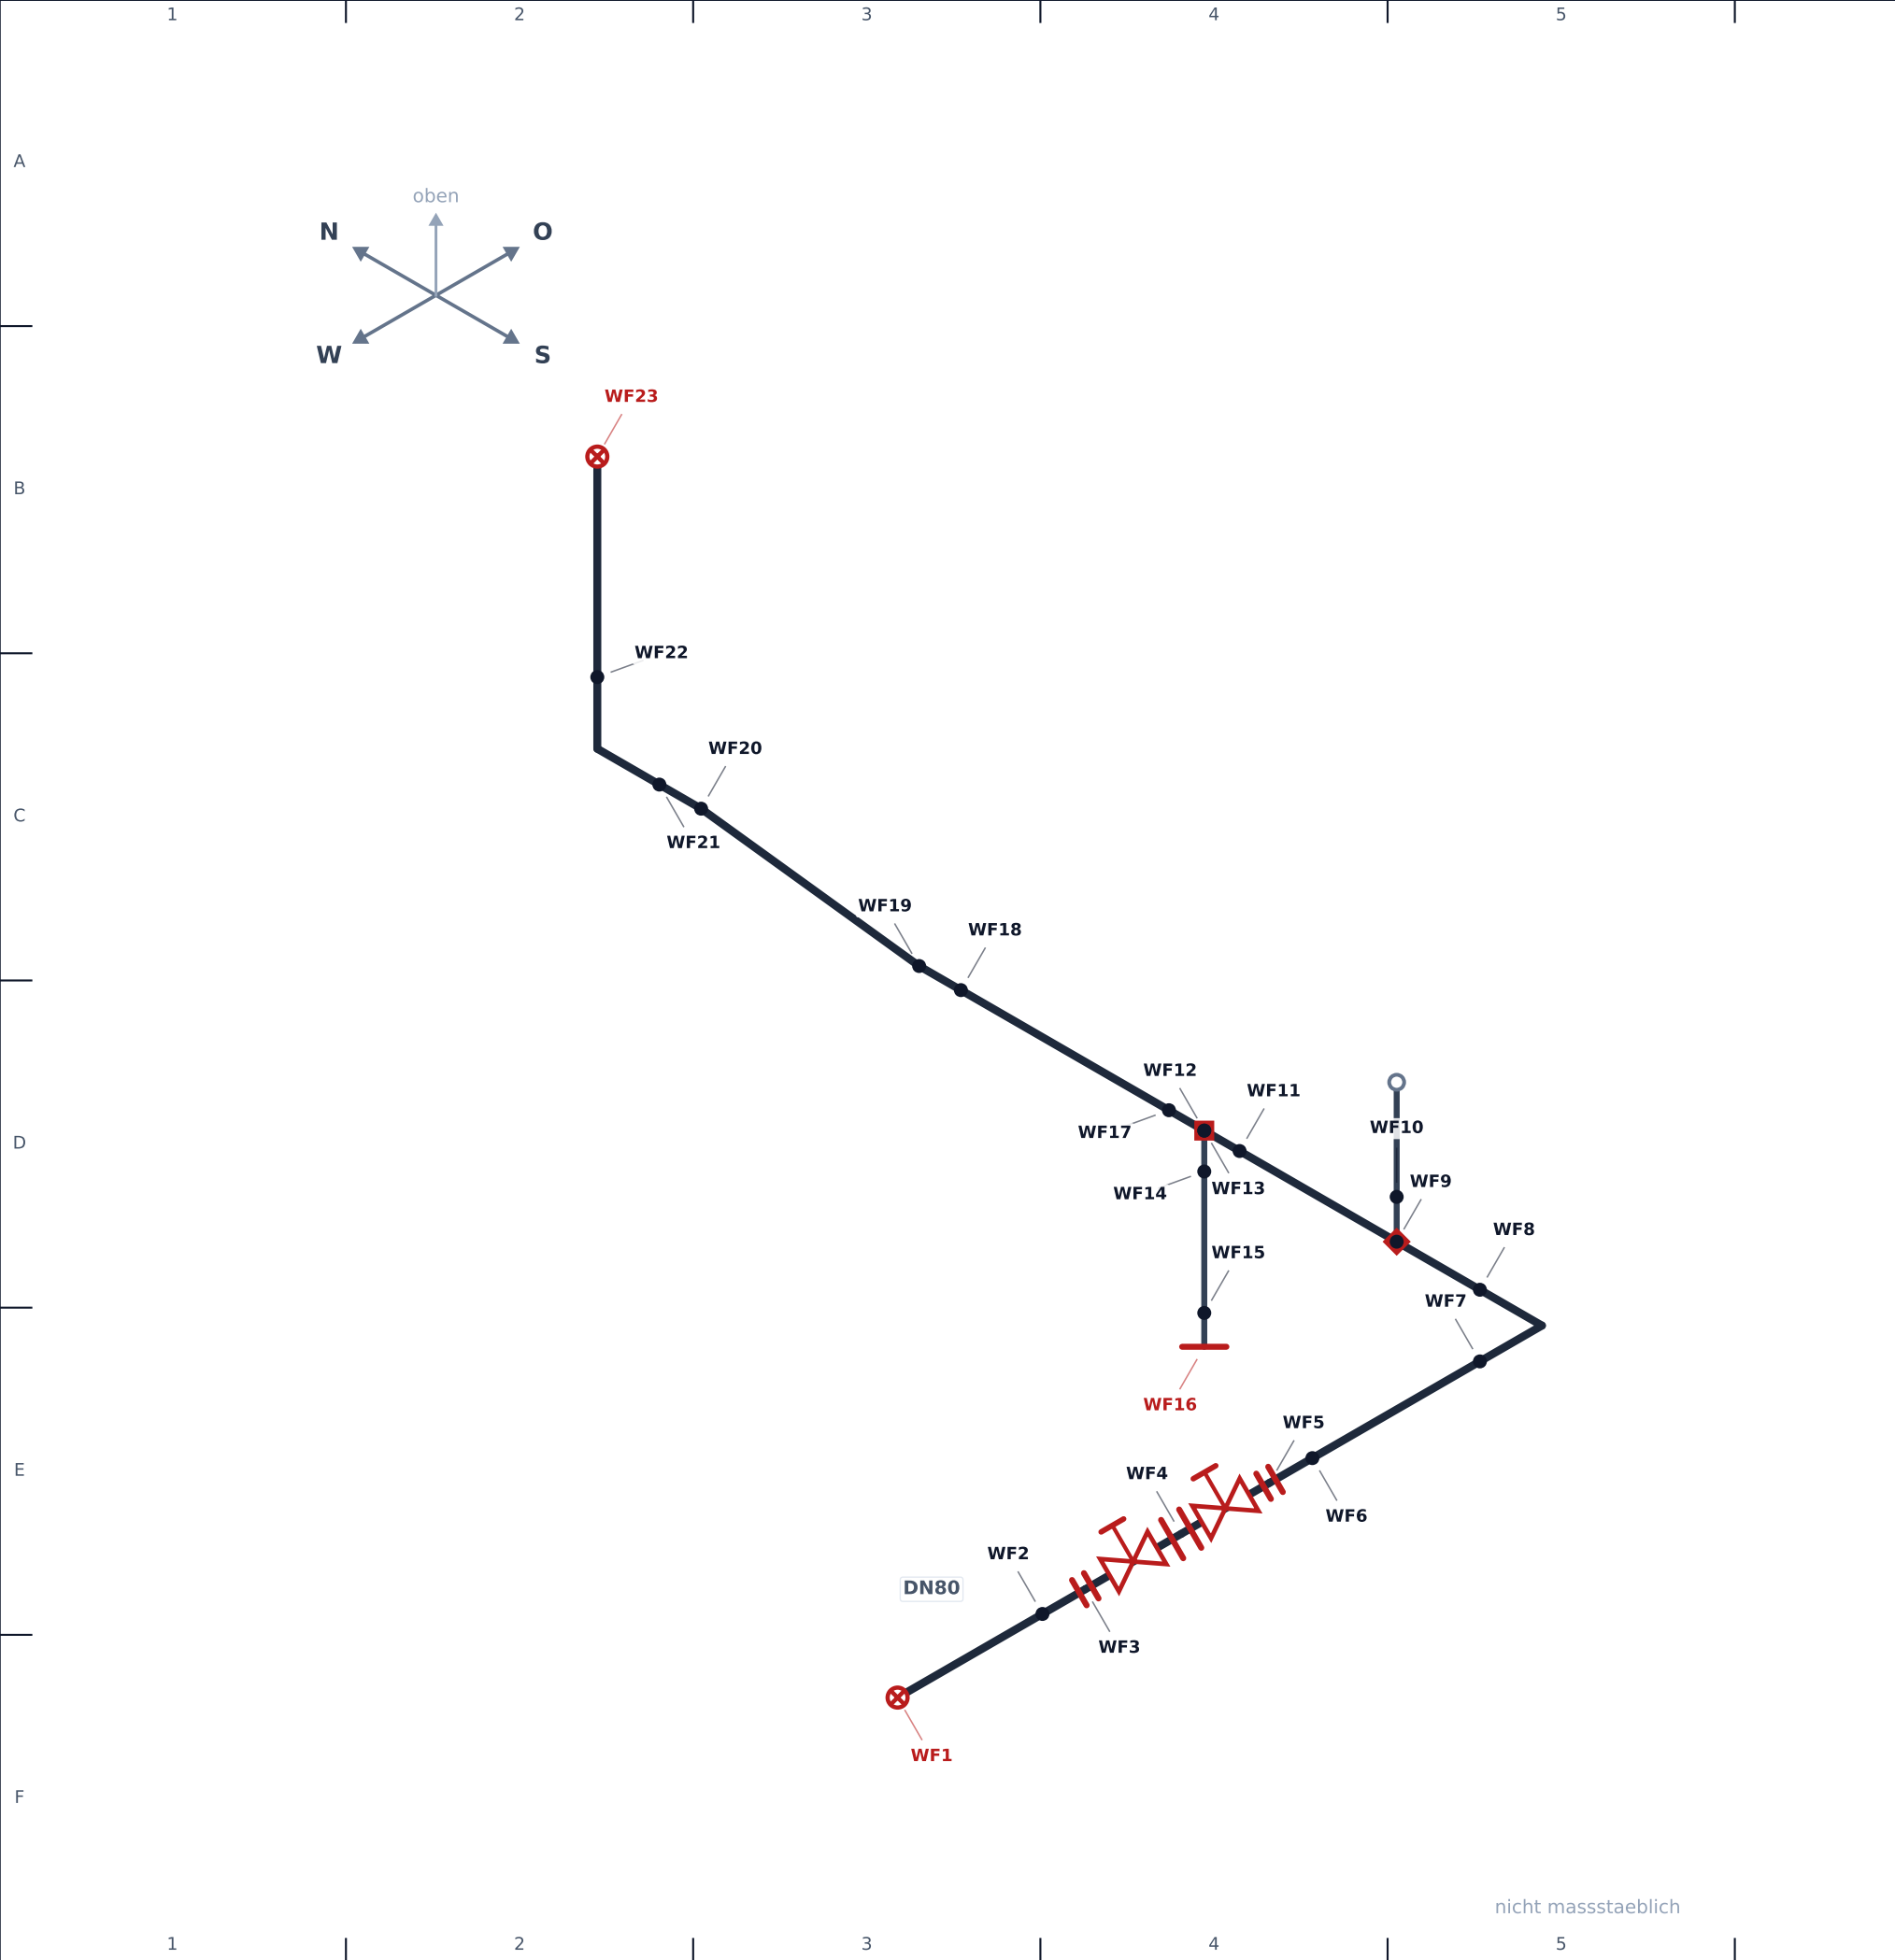

Stueckliste

Pos	Anzahl	Benennung	DN	Wand	Werkstoff	Norm
1	0.60 m	Rohr	50	3.91	P235GH	EN 10216-2
2	9.68 m	Rohr	80	5.49	P235GH	EN 10216-2
3	1 St	Anschweissstutzen	50	3.91	P235GH	MSS SP-97
4	2 St	Armatur mit Flanschen	80		P235GH	EN 558
5	2 St	Bogen 45 Grad	80	5.49	P235GH	EN 10253-2
6	2 St	Bogen 90	80	5.49	P235GH	EN 10253-2
7	1 St	T-Stueck	80	5.49	P235GH	EN 10253-2
8	1 St	T-Stueck (Abzweig)	80	5.49	P235GH	EN 10253-2

... 3 weitere Positionen - siehe Excel

Nahtliste

Naht	Art	DN	Ort	Wo
WF1	Rundnaht	80	Anschluss Anfang	Baustelle
WF2	Rundnaht	80	Rohr / Vorschweissflansch	Werkstatt
WF3	Flanschverbindung	80	Vorschweissflansch / Armatur mit Flanschen	Werkstatt
WF4	Flanschverbindung	80	Armatur mit Flanschen / Armatur mit Flansc...	Werkstatt
WF5	Flanschverbindung	80	Armatur mit Flanschen / Vorschweissflansch	Werkstatt
WF6	Rundnaht	80	Vorschweissflansch / Rohr	Werkstatt
WF7	Rundnaht	80	Rohr / Bogen 90	Werkstatt
WF8	Rundnaht	80	Bogen 90 / Rohr	Werkstatt
WF9	Rundnaht	50	Anschweissstutzen auf DN 80	Werkstatt
WF10	Rundnaht	50	Abzweigrohr angeschweisst	Werkstatt
WF11	Rundnaht	80	Rohr / T-Stueck	Werkstatt
WF12	Rundnaht	80	Fertig-T Durchgang 1	Werkstatt
WF13	Rundnaht	80	Fertig-T Durchgang 2	Werkstatt
WF14	Rundnaht	80	Abzweigrohr angeschweisst	Werkstatt
WF15	Rundnaht	80	Abzweig / Vorschweissflansch	Werkstatt
WF16	Flanschverbindung	80	Abzweig Flanschanschluss	Baustelle



... 7 weitere Naehnte - siehe Excel

Legende

- Werkstattnaht
- Baustellennaht
- Vorschweissflansch
- Armatur
- Fertig-T
- Anschweissstutzen
- Positionsnummer aus der Stueckliste

PipeCraft - Rohrfolge

Zeichnung ISO-1001	Leitung 80-PL-1001-P235GH
Projekt / Anlage Testanlage Nord	NPD DN 80
Werkstoff P235GH	Schedule STD
Auslegungsdruck 16 bar	Auslegungstemperatur 120 Grad C
Isolierung 60 mm MW	Rohr gesamt 11.93 m
Naehnte / Flansche 19 / 4	Baustellennaehnte 3
Erstellt von T. Brors	Datum / Ansicht 05.09.2026 · Schweiessen

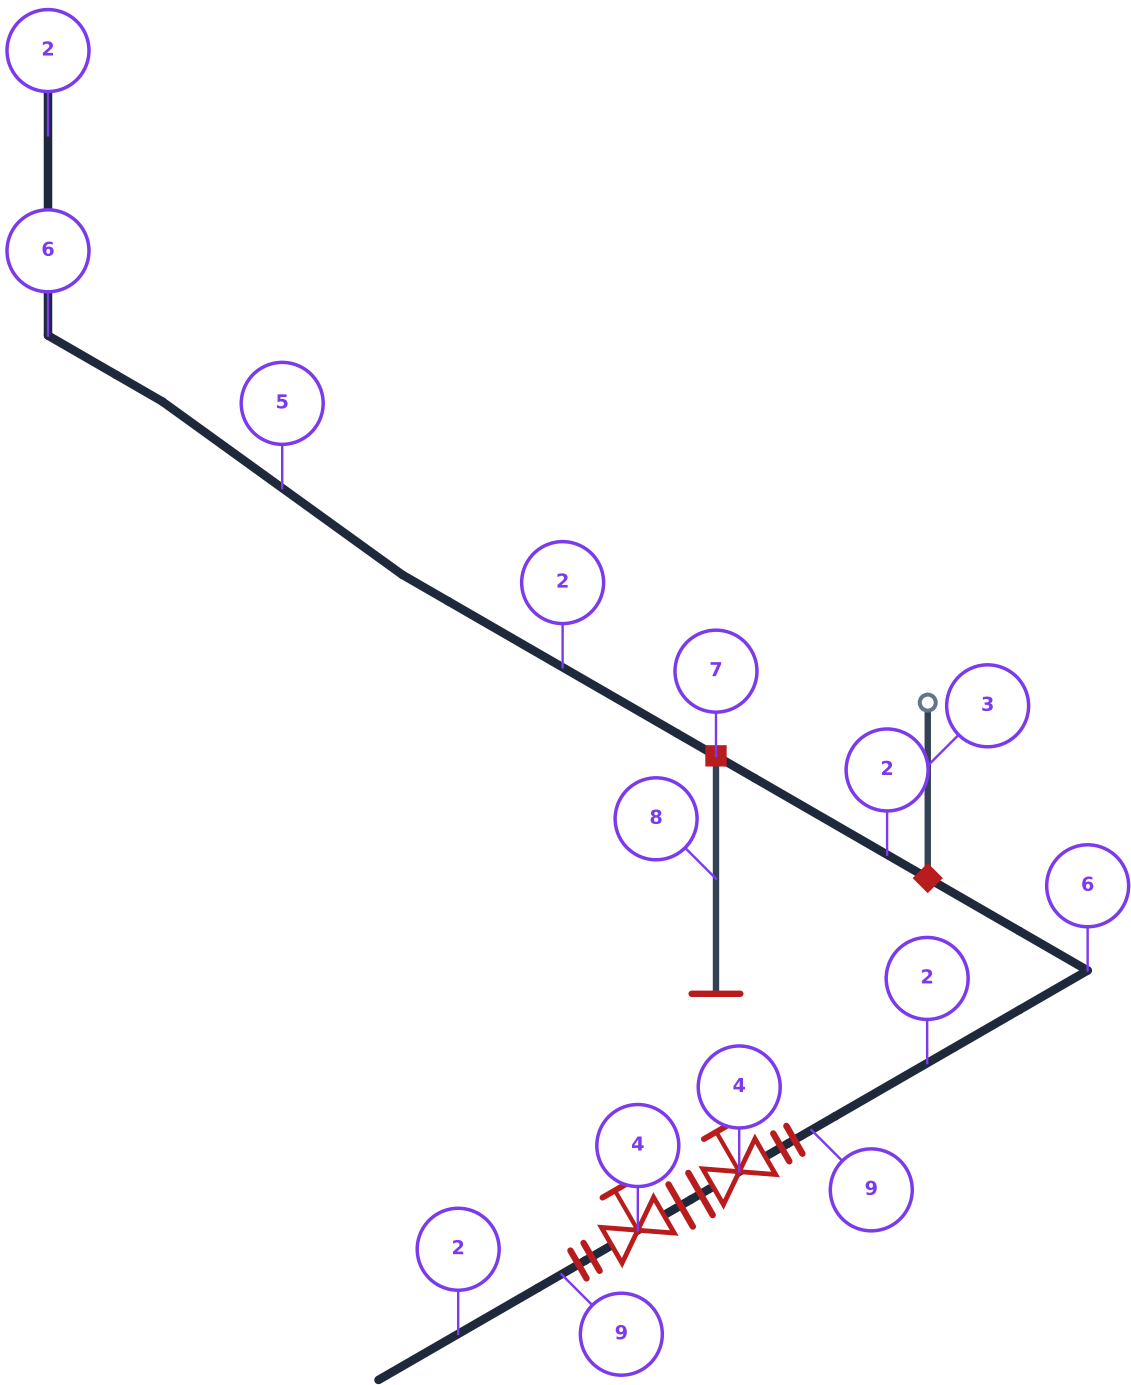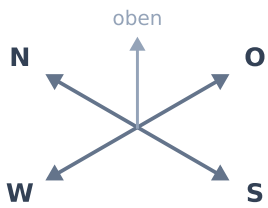

Stueckliste

Pos	Anzahl	Benennung	DN	Wand	Werkstoff	Norm
1	0.60 m	Rohr	50	3.91	P235GH	EN 10216-2
2	9.68 m	Rohr	80	5.49	P235GH	EN 10216-2
3	1 St	Anschweissstutzen	50	3.91	P235GH	MSS SP-97
4	2 St	Armatur mit Flanschen	80		P235GH	EN 558
5	2 St	Bogen 45 Grad	80	5.49	P235GH	EN 10253-2
6	2 St	Bogen 90	80	5.49	P235GH	EN 10253-2
7	1 St	T-Stueck	80	5.49	P235GH	EN 10253-2
8	1 St	T-Stueck (Abzweig)	80	5.49	P235GH	EN 10253-2

... 3 weitere Positionen - siehe Excel

Nahtliste

Naht	Art	DN	Ort	Wo
WF1	Rundnaht	80	Anschluss Anfang	Baustelle
WF2	Rundnaht	80	Rohr / Vorschweissflansch	Werkstatt
WF3	Flanschverbindung	80	Vorschweissflansch / Armatur mit Flanschen	Werkstatt
WF4	Flanschverbindung	80	Armatur mit Flanschen / Armatur mit Flansc...	Werkstatt
WF5	Flanschverbindung	80	Armatur mit Flanschen / Vorschweissflansch	Werkstatt
WF6	Rundnaht	80	Vorschweissflansch / Rohr	Werkstatt
WF7	Rundnaht	80	Rohr / Bogen 90	Werkstatt
WF8	Rundnaht	80	Bogen 90 / Rohr	Werkstatt
WF9	Rundnaht	50	Anschweissstutzen auf DN 80	Werkstatt
WF10	Rundnaht	50	Abzweigrohr angeschweisst	Werkstatt
WF11	Rundnaht	80	Rohr / T-Stueck	Werkstatt
WF12	Rundnaht	80	Fertig-T Durchgang 1	Werkstatt
WF13	Rundnaht	80	Fertig-T Durchgang 2	Werkstatt
WF14	Rundnaht	80	Abzweigrohr angeschweisst	Werkstatt
WF15	Rundnaht	80	Abzweig / Vorschweissflansch	Werkstatt
WF16	Flanschverbindung	80	Abzweig Flanschanschluss	Baustelle

... 7 weitere Naehnte - siehe Excel

Legende

- Werkstattnaht
- Baustellennaht
- Vorschweissflansch
- Armatur
- Fertig-T
- Anschweissstutzen
- Positionsnummer aus der Stueckliste

PipeCraft - Rohrfolge

Zeichnung ISO-1001	Leitung 80-PL-1001-P235GH
Projekt / Anlage Testanlage Nord	NPD DN 80
Werkstoff P235GH	Schedule STD
Auslegungsdruck 16 bar	Auslegungstemperatur 120 Grad C
Isolierung 60 mm MW	Rohr gesamt 11.93 m
Naehnte / Flansche 19 / 4	Baustellennaehnte 3
Erstellt von T. Brors	Datum / Ansicht 05.09.2026 · Montage