


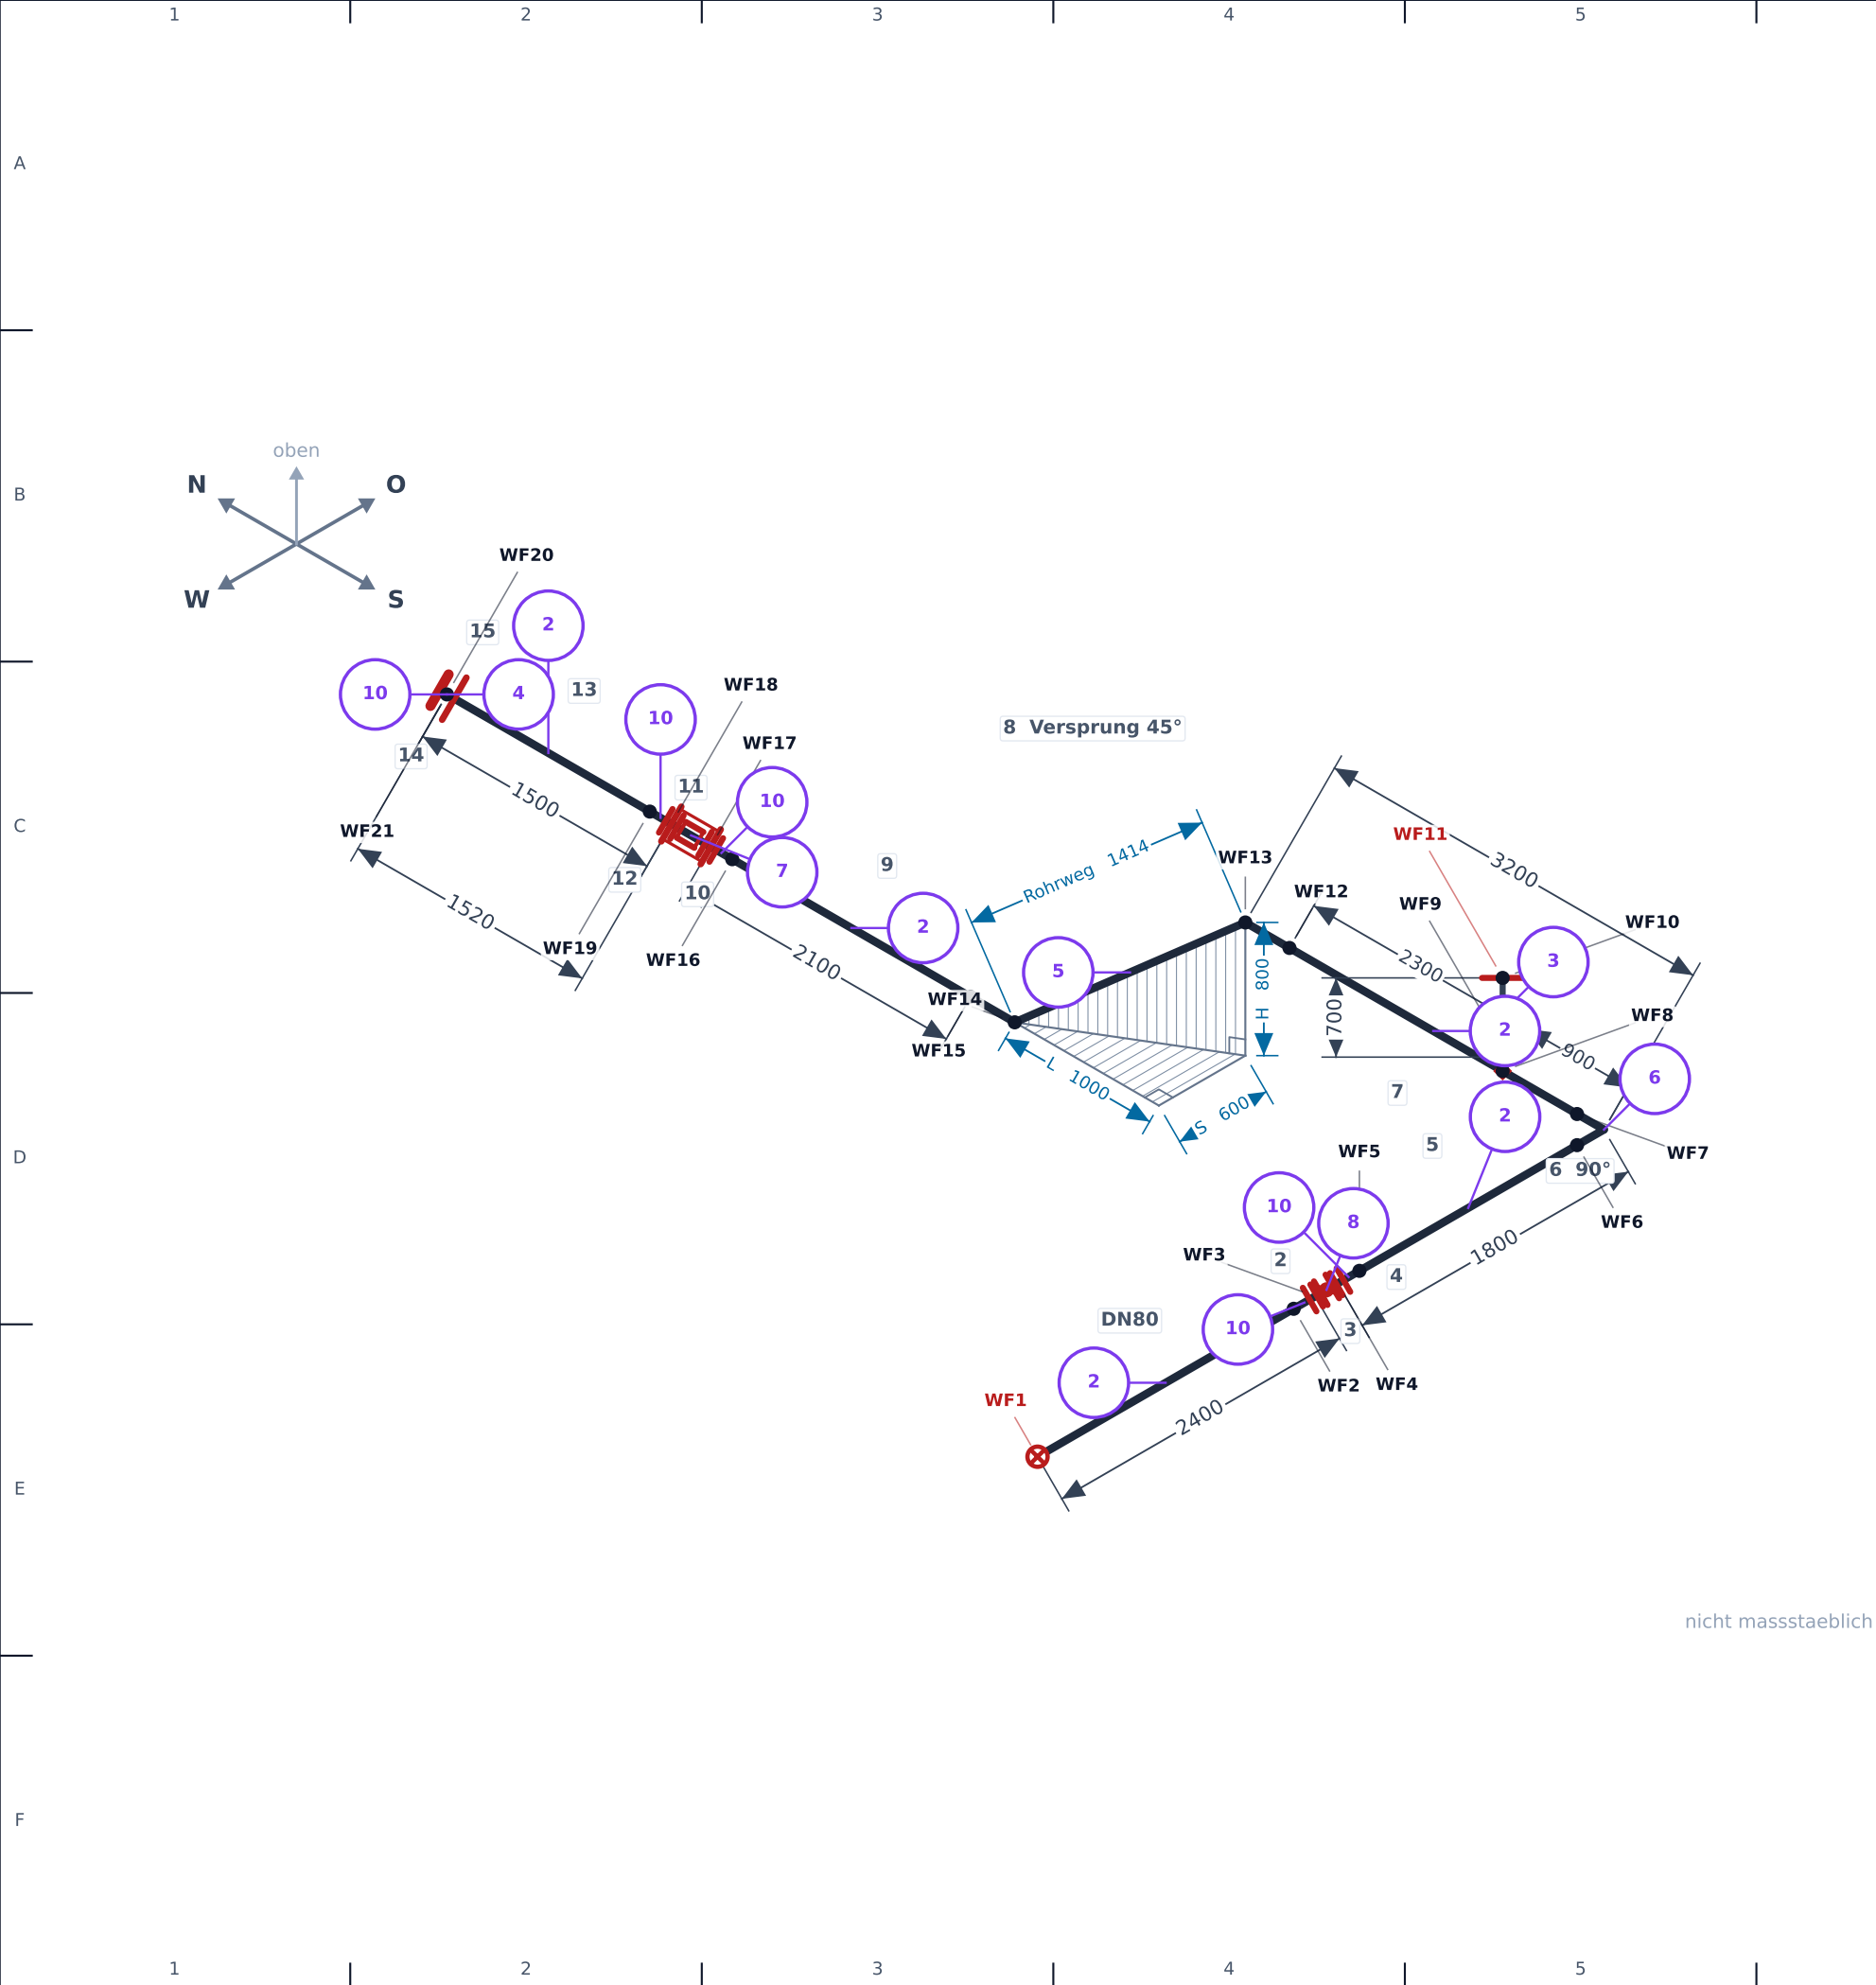

Stueckliste

Pos	Anzahl	Benennung	DN	Wand	Werkstoff	Norm
1	0.62 m	Rohr	50	3.91	P235GH	EN 10216-2
2	11.75 m	Rohr	80	5.49	P235GH	EN 10216-2
3	1 St	Anschweissstutzen	50	3.91	P235GH	MSS SP-97
4	1 St	Blindflansch	80		P235GH	EN 1092-1 Typ 05
5	2 St	Bogen 45 Grad	80	5.49	P235GH	EN 10253-2
6	1 St	Bogen 90	80	5.49	P235GH	EN 10253-2
7	1 St	Demontagestueck	80		P235GH	Herstellerangabe
8	1 St	Klappe	80		P235GH	EN 593 / EN 558
9	1 St	Vorschweissflansch	50	3.91	P235GH	EN 1092-1 Typ 11

... 6 weitere Positionen - siehe Excel

Nahtliste

Naht	Art	DN	Ort
WF1	Rundnaht	80	Anschluss Anfang
WF2	Rundnaht	80	Rohr / Vorschweissflansch
WF3	Flanschverbindung	80	Vorschweissflansch / Klappe
WF4	Flanschverbindung	80	Klappe / Vorschweissflansch
WF5	Rundnaht	80	Vorschweissflansch / Rohr
WF6	Rundnaht	80	Rohr / Bogen 90
WF7	Rundnaht	80	Bogen 90 / Rohr
WF8	Rundnaht	50	Anschweissstutzen auf DN 80
WF9	Rundnaht	50	Abzweigrohr angeschweisst
WF10	Rundnaht	50	Abzweig / Vorschweissflansch
WF11	Flanschverbindung	50	Abzweig Flanschanschluss
WF12	Rundnaht	80	Rohr / Versprung
WF13	Rundnaht	80	Bogen / Schraegrohr

... 8 weitere Naehnte - siehe Excel

Legende

- Werkstattnaht
- Baustellennaht
- Vorschweissflansch
- Armatur
- Klappe (Zwischenflansch)
- Demontagestueck
- Fertig-T
- Anschweissstutzen
- Positionsnummer aus der Stueckliste

PipeCraft - Rohrfolge

Zeichnung ISO-1001	Leitung 80-PL-1001
Projekt / Anlage PipeCraft Beispiel	NPD DN 80
Werkstoff P235GH	Schedule STD
Auslegungsdruck 16 bar	Auslegungstemperatur -
Isolierung -	Rohr gesamt 13.50 m
Naehnte / Flansche 15 / 6	Baustellennaehnte 2
Erstellt von PipeCraft	Datum / Ansicht - - Alles