


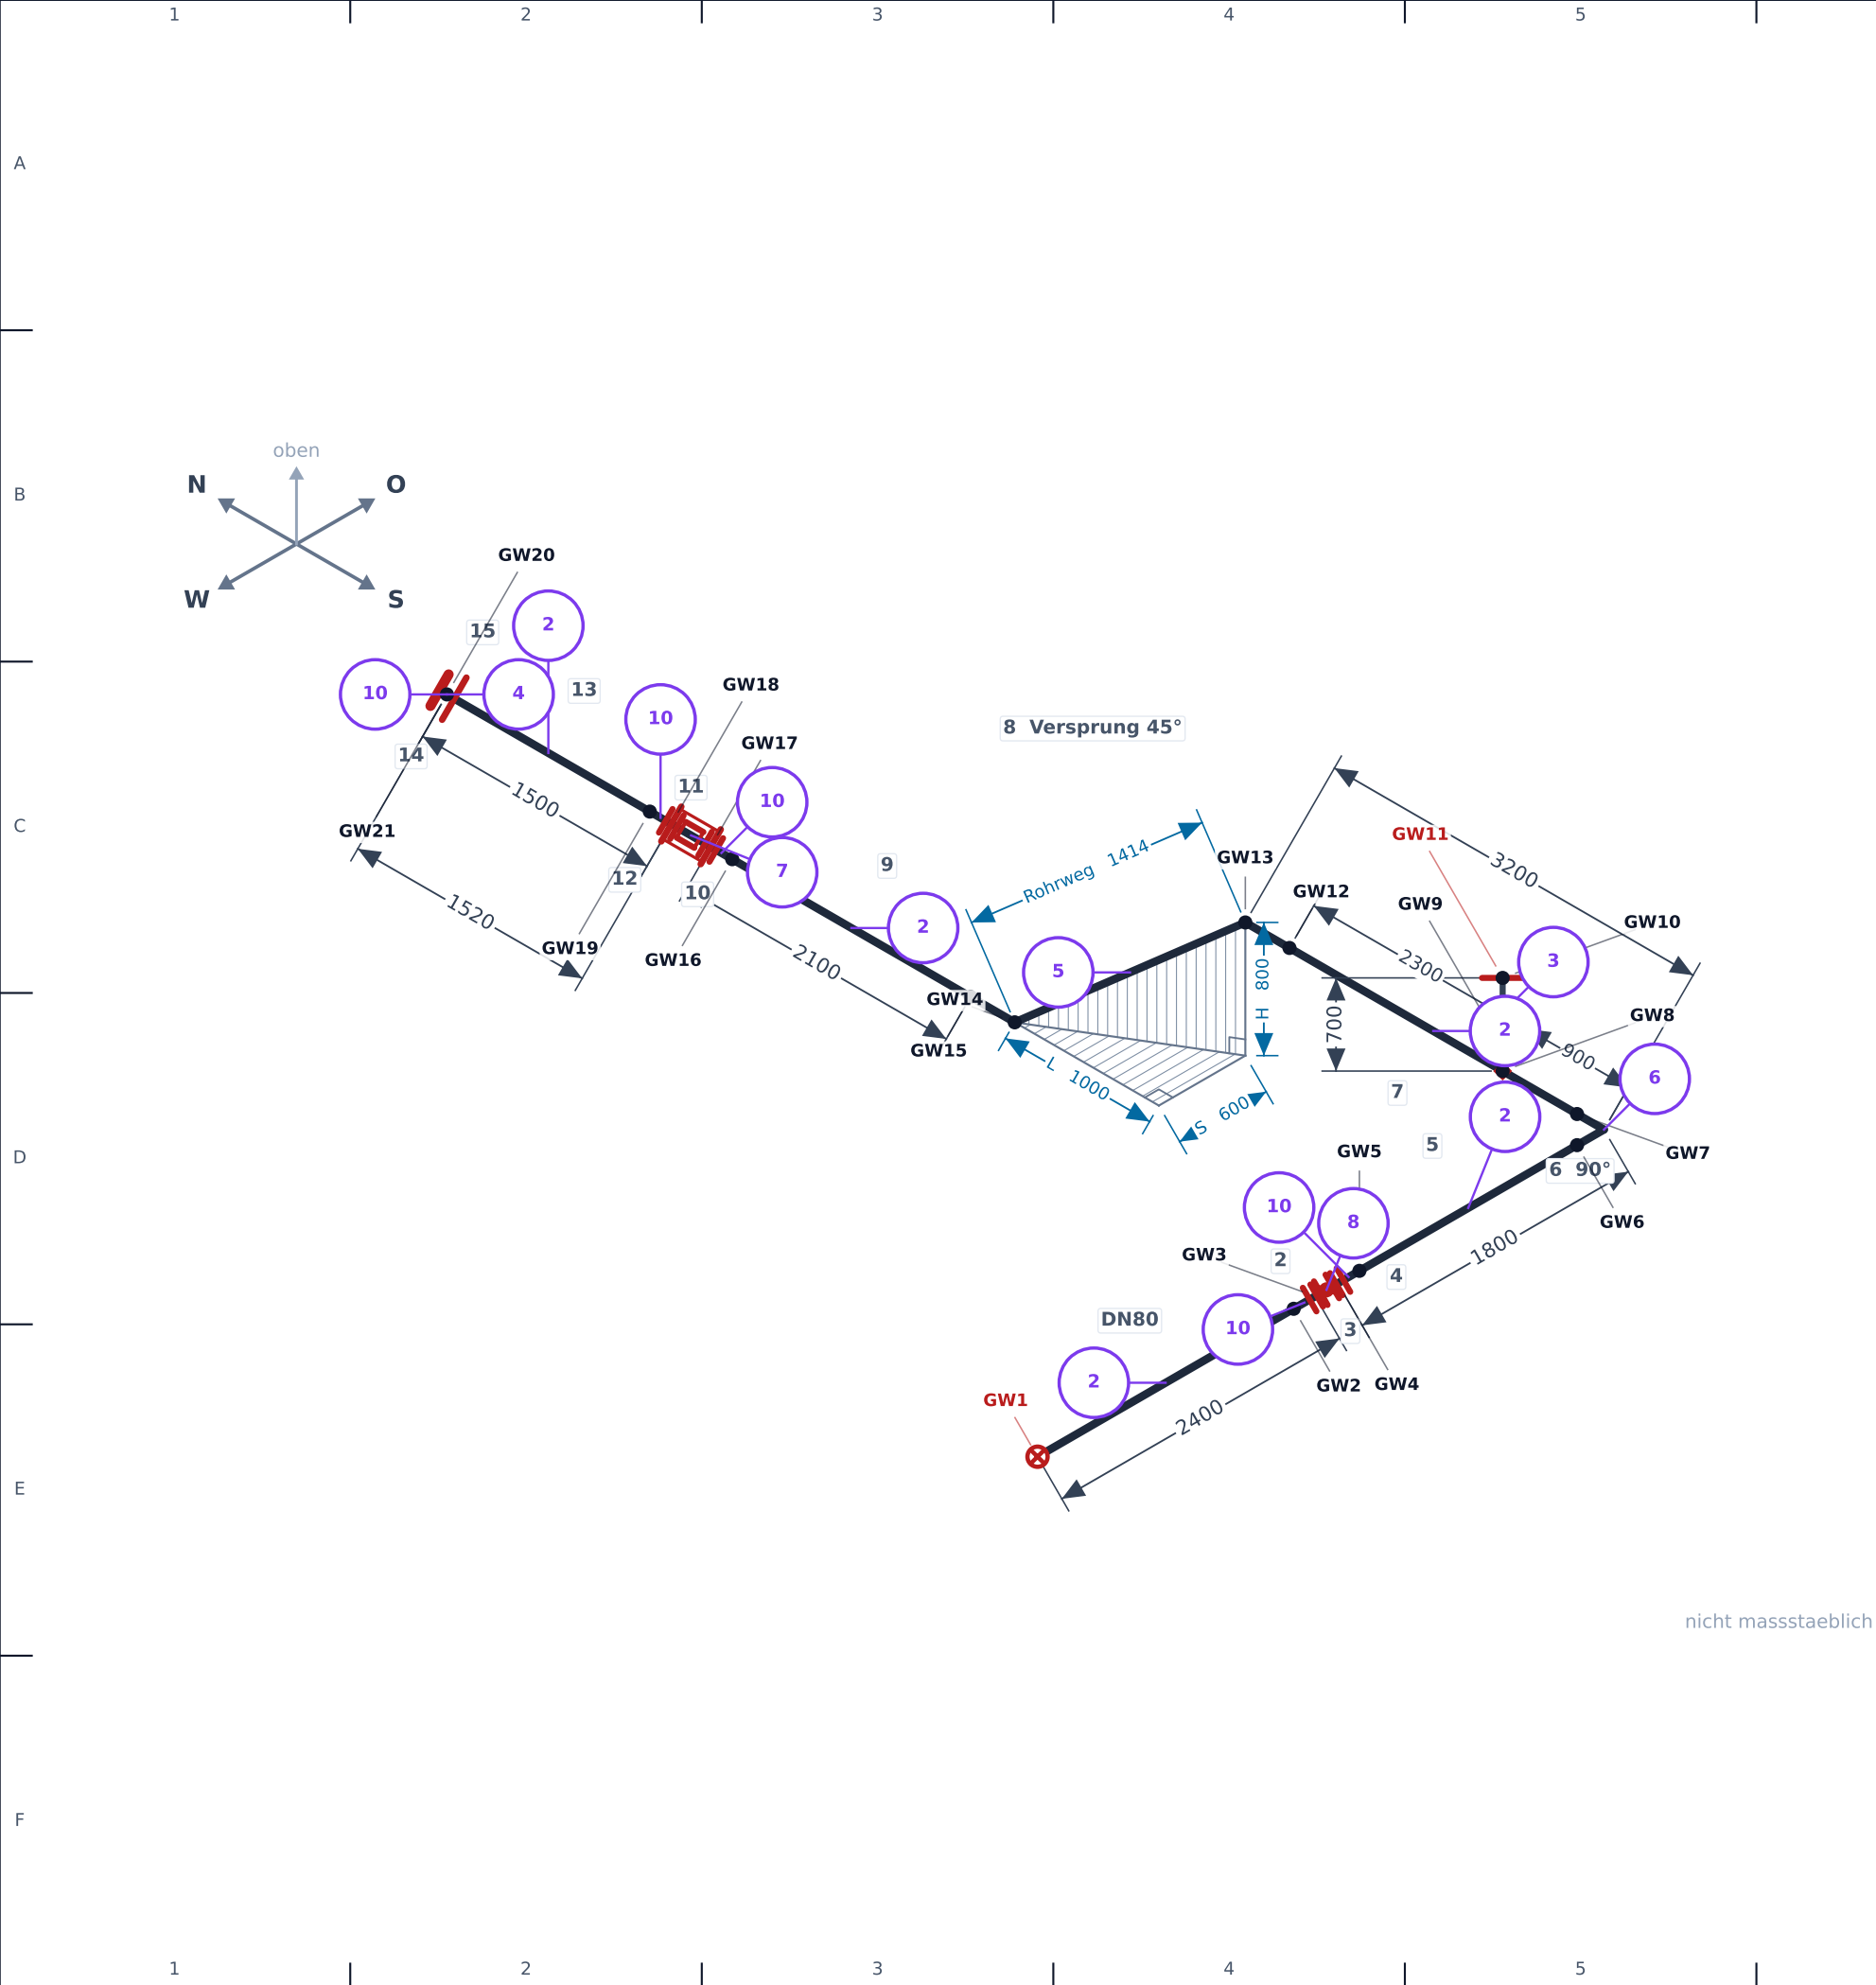

Stueckliste						
Pos	Anzahl	Benennung	DN	Wand	Werkstoff	Norm
1	0.62 m	Rohr	50	3.91	P235GH	EN 10216-2
2	11.75 m	Rohr	80	5.49	P235GH	EN 10216-2
3	1 St	Anschweissstutzen	50	3.91	P235GH	MSS SP-97
4	1 St	Blindflansch	80		P235GH	EN 1092-1 Typ 05
5	2 St	Bogen 45 Grad	80	5.49	P235GH	EN 10253-2
6	1 St	Bogen 90	80	5.49	P235GH	EN 10253-2
7	1 St	Demontagestueck	80		P235GH	Herstellerangabe
8	1 St	Klappe	80		P235GH	EN 593 / EN 558
9	1 St	Vorschweissflansch	50	3.91	P235GH	EN 1092-1 Typ 11

... 6 weitere Positionen - siehe Excel

Nahtliste				
Naht	Art	DN	Ort	Schweisser
GW1	Rundnaht	80	Anschluss Anfang	
GW2	Rundnaht	80	Rohr / Vorschweissflansch	
GW3	Flanschverbindung	80	Vorschweissflansch / Klappe	
GW4	Flanschverbindung	80	Klappe / Vorschweissflansch	
GW5	Rundnaht	80	Vorschweissflansch / Rohr	
GW6	Rundnaht	80	Rohr / Bogen 90	
GW7	Rundnaht	80	Bogen 90 / Rohr	
GW8	Rundnaht	50	Anschweissstutzen auf DN 80	
GW9	Rundnaht	50	Abzweigrohr angeschweisst	
GW10	Rundnaht	50	Abzweig / Vorschweissflansch	
GW11	Flanschverbindung	50	Abzweig Flanschanschluss	
GW12	Rundnaht	80	Rohr / Versprung	
GW13	Rundnaht	80	Bogen / Schraegrohr	

... 8 weitere Naehnte - siehe Excel

Legende	
●	Werkstattnaht
⊗	Baustellennaht
	Vorschweissflansch
X	Armatur
Z	Klappe (Zwischenflansch)
=	Demontagestueck
■	Fertig-T
◆	Anschweissstutzen
○	Positionsnummer aus der Stueckliste

PipeCraft - Rohrfolge	
Zeichnung ISO-1001	Leitung 80-PL-1001
Projekt / Anlage PipeCraft Beispiel	NPD DN 80
Werkstoff P235GH	Schedule STD
Auslegungsdruck 16 bar	Auslegungstemperatur -
Isolierung -	Rohr gesamt 13.50 m
Naehnte / Flansche 15 / 6	Baustellennaehnte 2
Erstellt von PipeCraft	Datum / Ansicht - · Alles