


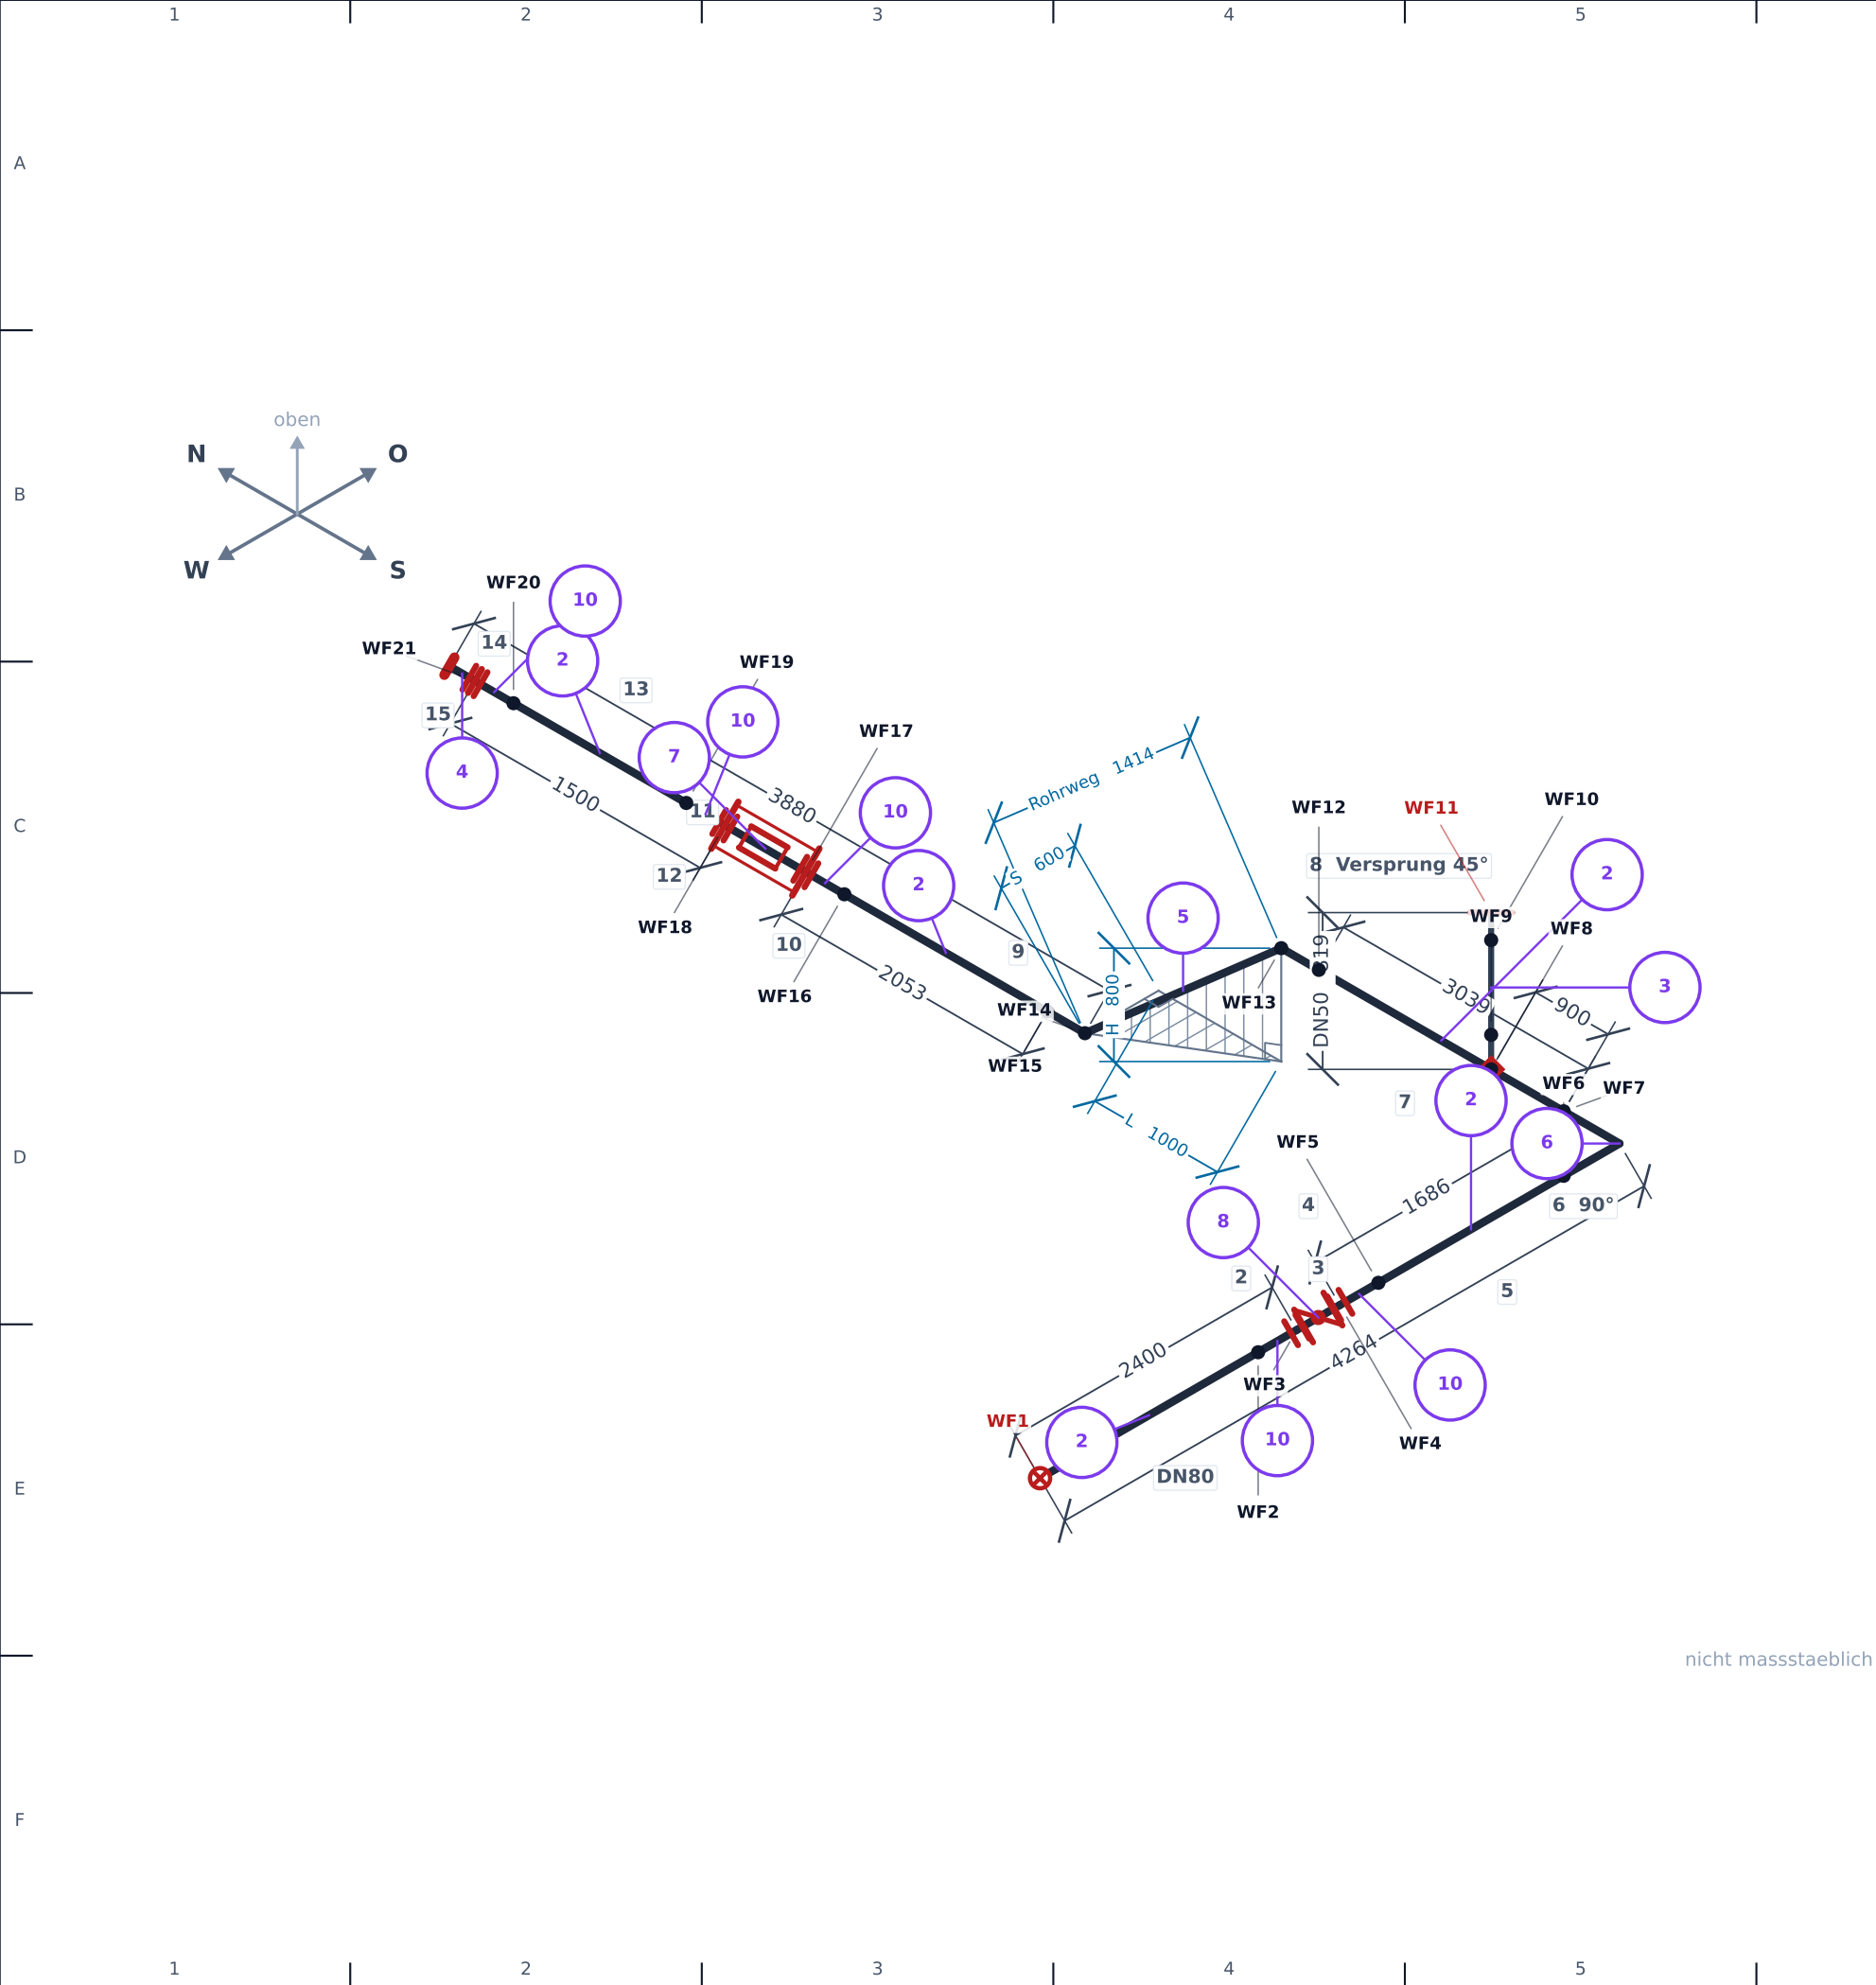

Stueckliste						
Pos	Anzahl	Benennung	DN	Wand	Werkstoff	Norm
1	0.70 m	Rohr	50	3.91	P235GH	EN 10216-2
2	11.75 m	Rohr	80	5.49	P235GH	EN 10216-2
3	1 St	Anschweissstutzen	50	3.91	P235GH	MSS SP-97
4	1 St	Blindflansch	80		P235GH	EN 1092-1 Typ 05
5	2 St	Bogen 45 Grad	80	5.49	P235GH	EN 10253-2
6	1 St	Bogen 90	80	5.49	P235GH	EN 10253-2
7	1 St	Demontagestueck	80		P235GH	Herstellerangabe
8	1 St	Klappe	80		P235GH	EN 593 / EN 558
9	1 St	Vorschweissflansch	50	3.91	P235GH	EN 1092-1 Typ 11

... 6 weitere Positionen - siehe Excel

Nahtliste				
Naht	Art	DN	Ort	Wo
WF1	Rundnaht	80	Anschluss Anfang	Baustelle
WF2	Rundnaht	80	Rohr / Vorschweissflansch	Werkstatt
WF3	Flanschverbindung	80	Vorschweissflansch / Klappe	Werkstatt
WF4	Flanschverbindung	80	Klappe / Vorschweissflansch	Werkstatt
WF5	Rundnaht	80	Vorschweissflansch / Rohr	Werkstatt
WF6	Rundnaht	80	Rohr / Bogen 90	Werkstatt
WF7	Rundnaht	80	Bogen 90 / Rohr	Werkstatt
WF8	Rundnaht	50	Anschweissstutzen auf DN 80	Werkstatt
WF9	Rundnaht	50	Abzweigrohr angeschweisst	Werkstatt
WF10	Rundnaht	50	Abzweig / Vorschweissflansch	Werkstatt
WF11	Flanschverbindung	50	Abzweig Flanschanschluss	Baustelle
WF12	Rundnaht	80	Rohr / Versprung	Werkstatt
WF13	Rundnaht	80	Bogen / Schraegrohr	Werkstatt

... 8 weitere Naehnte - siehe Excel

Legende	
●	Werkstattnaht
⊗	Baustellennaht
	Vorschweissflansch
X	Armatur
Z	Klappe (Zwischenflansch)
=	Demontagestueck
■	Fertig-T
◆	Anschweissstutzen
○	Positionsnummer aus der Stueckliste

PipeCraft - Rohrfolge	
Zeichnung ISO-1001	Leitung 80-PL-1001
Projekt / Anlage PipeCraft Beispiel	NPD DN 80
Werkstoff P235GH	Schedule STD
Auslegungsdruck 16 bar	Auslegungstemperatur -
Isolierung -	Rohr gesamt 13.58 m
Naehnte / Flansche 15 / 6	Baustellennaehnte 2
Erstellt von PipeCraft	Datum / Ansicht - / Alles