
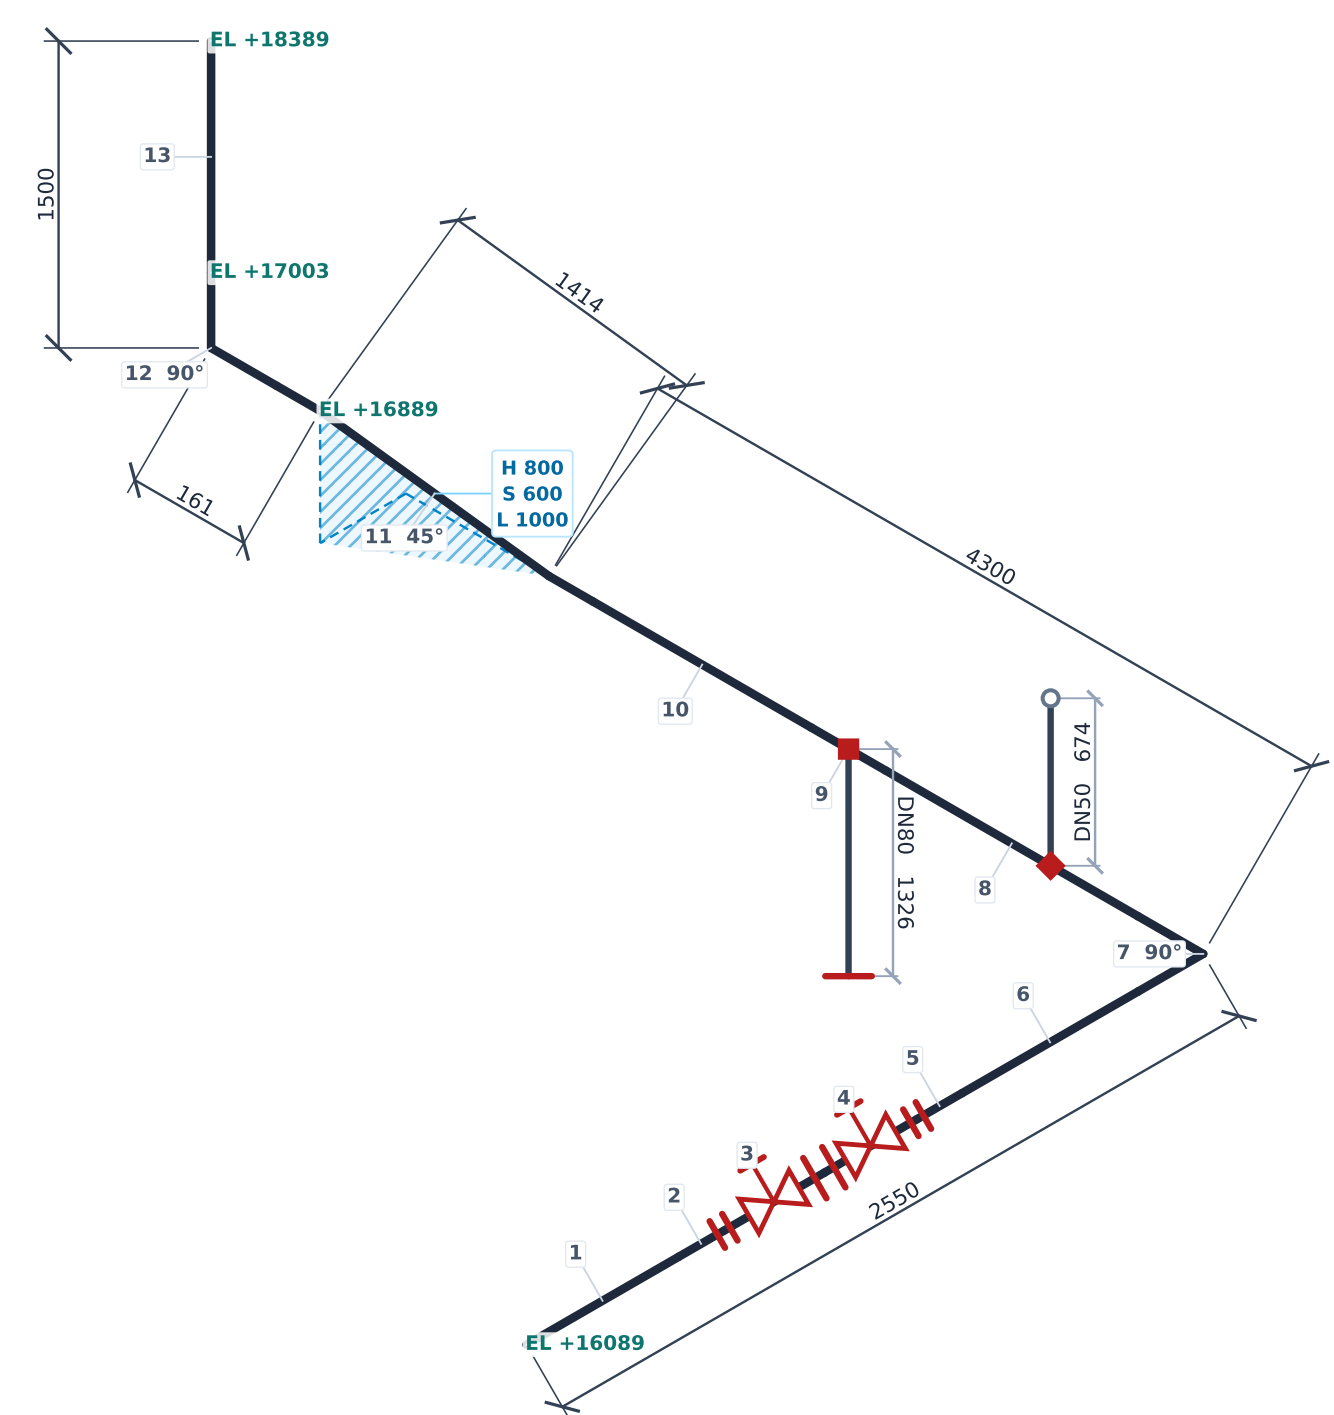


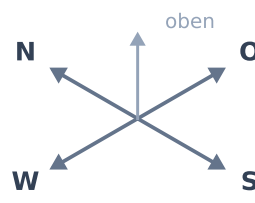

nicht massstaeblich

Stueckliste

Pos	Anzahl	Benennung	DN	Wand	Werkstoff	Norm
1	0.60 m	Rohr	50	3.91	P235GH	EN 10216-2
2	9.68 m	Rohr	80	5.49	P235GH	EN 10216-2
3	1 St	Anschweissstutzen	50	3.91	P235GH	MSS SP-97
4	2 St	Armatur mit Flanschen	80		P235GH	EN 558
5	2 St	Bogen 45 Grad	80	5.49	P235GH	EN 10253-2
6	2 St	Bogen 90	80	5.49	P235GH	EN 10253-2

... 5 weitere Positionen - siehe Excel

Nahtliste

Naht	Art	DN	Ort	Wo
WF1	Rundnaht	80	Anschluss Anfang	Baustelle
WF2	Rundnaht	80	Rohr / Vorschweissflansch	Werkstatt
WF3	Flanschverbindung	80	Vorschweissflansch / Armatur mit Flanschen	Werkstatt
WF4	Flanschverbindung	80	Armatur mit Flanschen / Armatur mit Flansc...	Werkstatt
WF5	Flanschverbindung	80	Armatur mit Flanschen / Vorschweissflansch	Werkstatt
WF6	Rundnaht	80	Vorschweissflansch / Rohr	Werkstatt
WF7	Rundnaht	80	Rohr / Bogen 90	Werkstatt
WF8	Rundnaht	80	Bogen 90 / Rohr	Werkstatt
WF9	Rundnaht	50	Anschweissstutzen auf DN 80	Werkstatt
WF10	Rundnaht	50	Abzweigrohr angeschweisst	Werkstatt

... 13 weitere Naehfte - siehe Excel

Halterungen


Halterung	Art	An Bauteil	Bei (mm)	Lage
FP1	Festpunkt	1	400	unten
GL1	Gleitlager	8	1200	unten
RS1	Rohrschelle	13	900	seitlich

Legende

- Werkstattnaht
- ⊗ Baustellennaht
- | Vorschweissflansch
- ✕ Armatur
- Fertig-T
- ◆ Anschweissstutzen
- Halterung, gefuellte = Festpunkt
- Positionsnummer aus der Stueckliste

PipeCraft - Rohrfolge

Zeichnung ISO-1001	Leitung 80-PL-1001-P235GH
Projekt / Anlage Testanlage Nord	NPD DN 80
Werkstoff P235GH	Schedule STD
Auslegungsdruck 16 bar	Auslegungstemperatur 120 Grad C
Isolierung 60 mm MW	Rohr gesamt 11.93 m
Naehfte / Flansche 19 / 4	Baustellennaehfte 3
Erstellt von T. Brors	Datum / Ansicht 04.09.2026 · Aufmass & Saegen

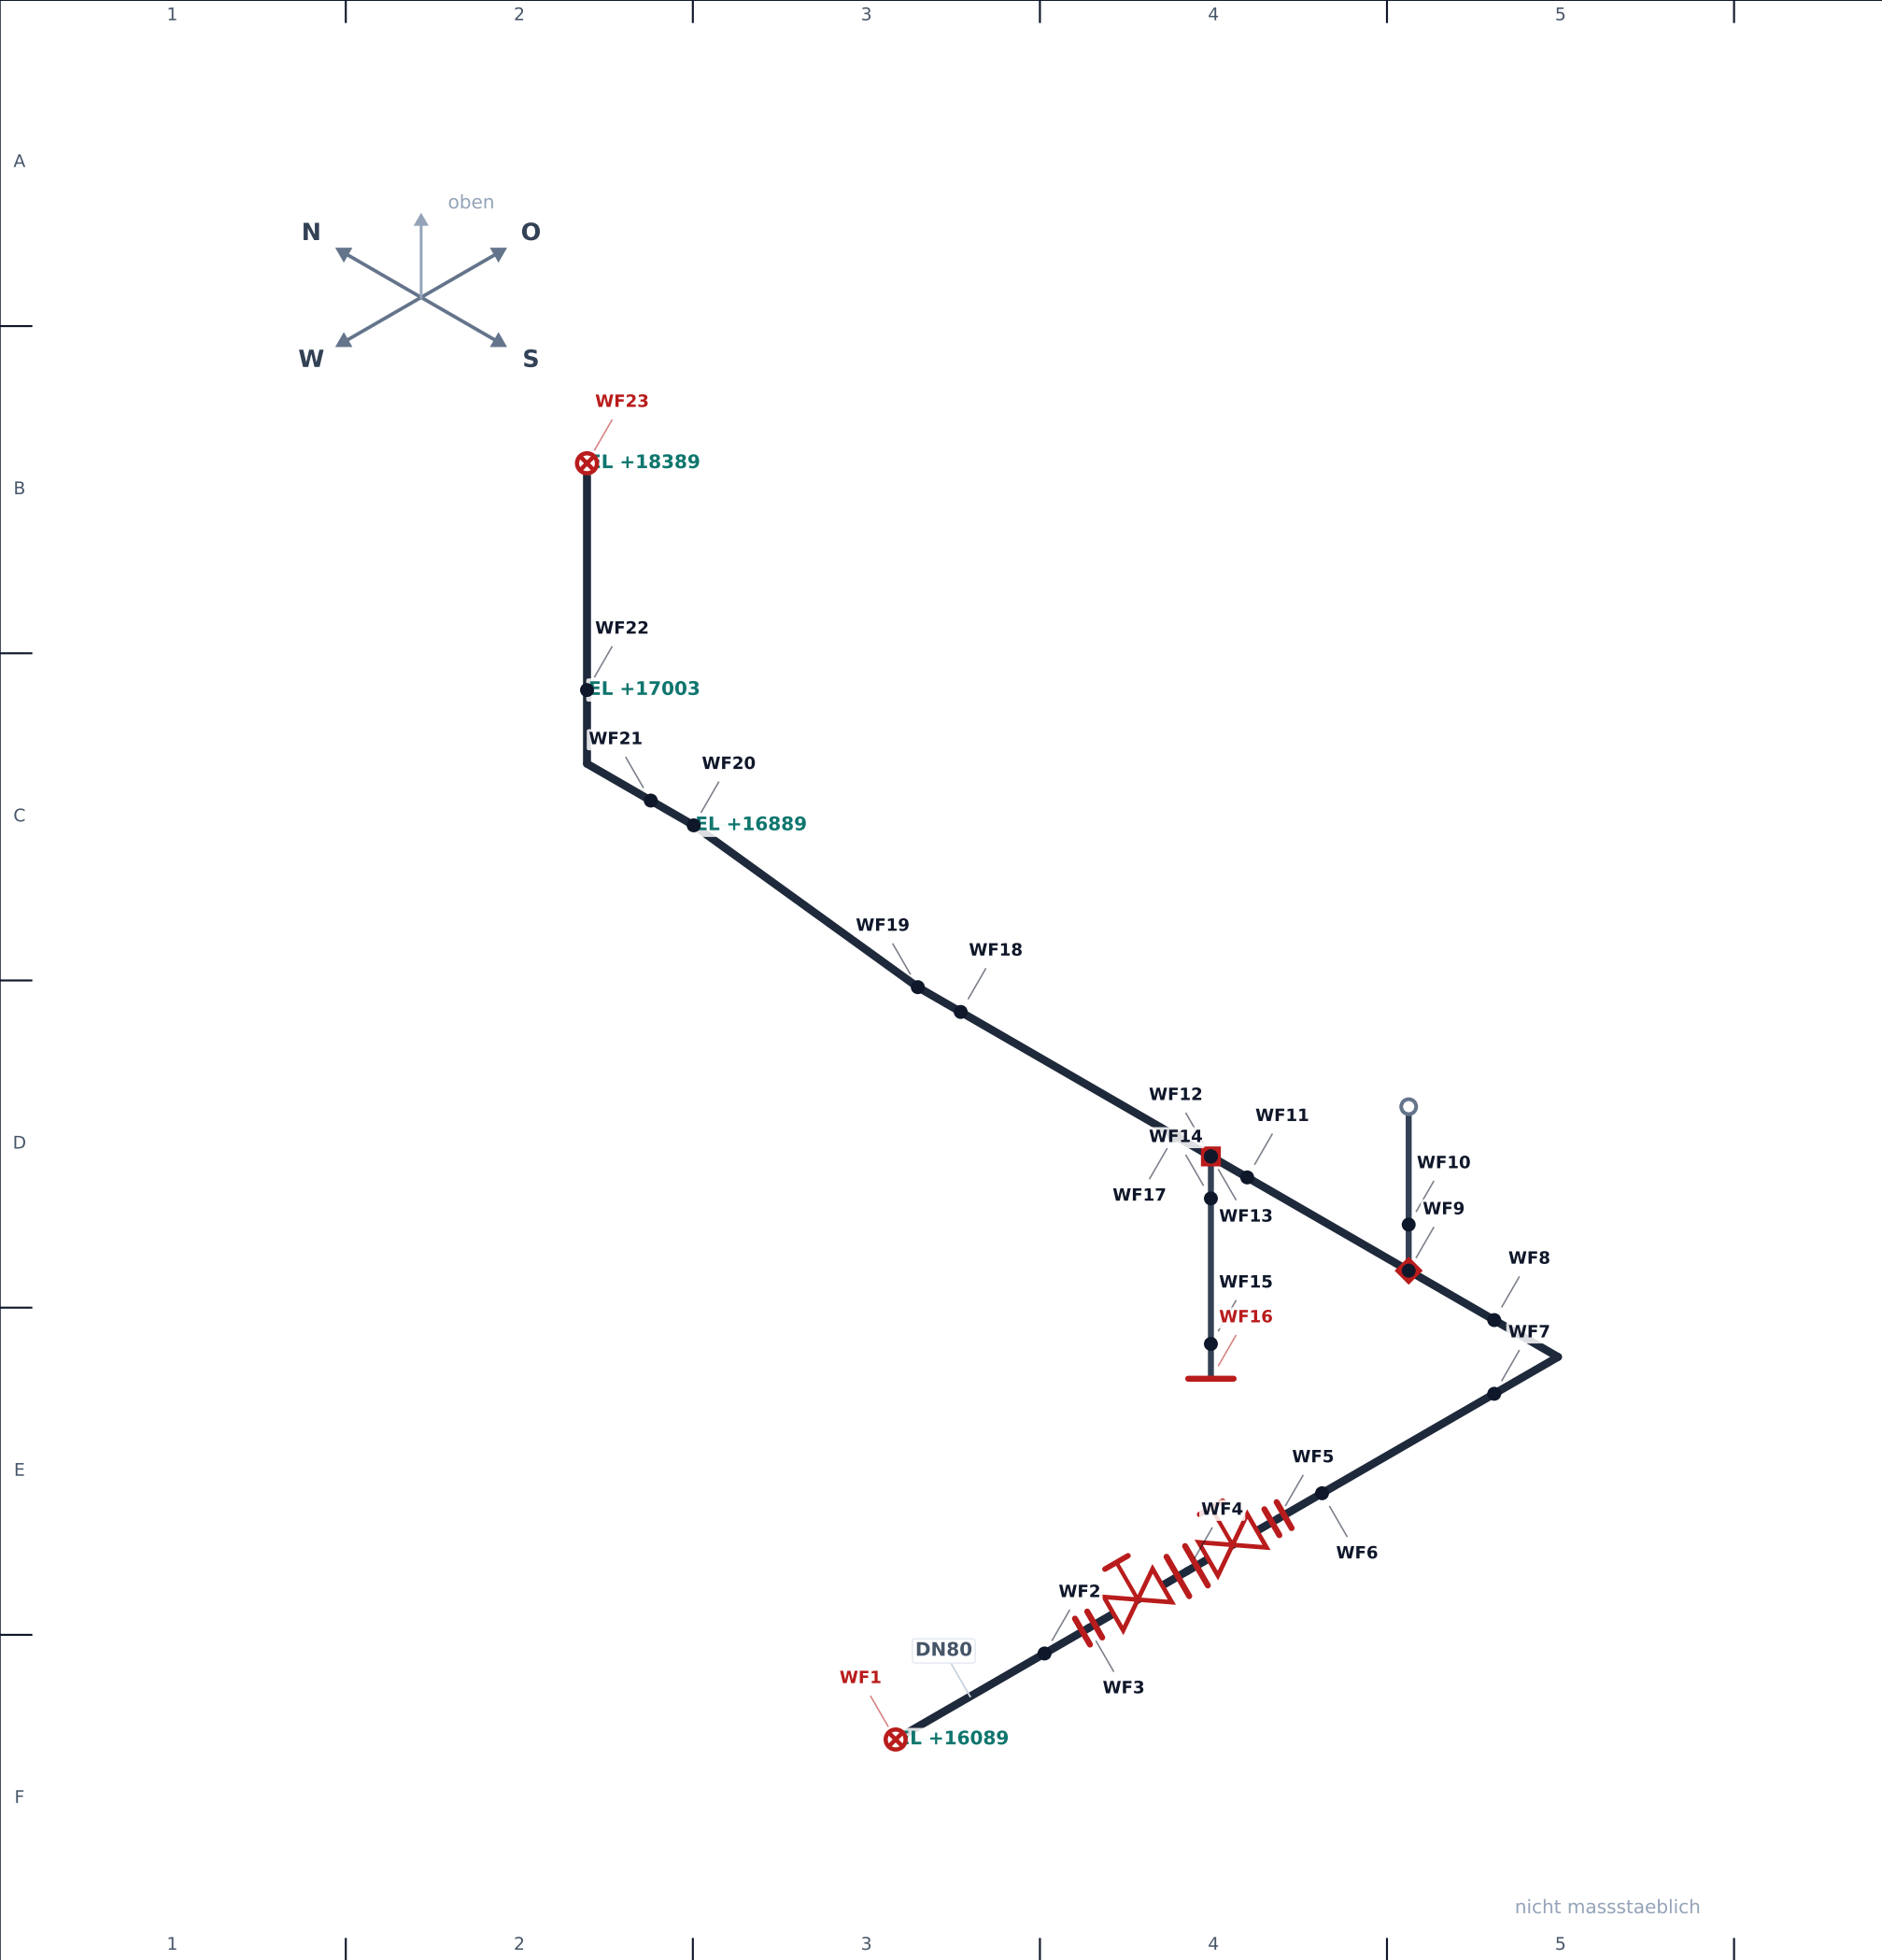

Stueckliste

Pos	Anzahl	Benennung	DN	Wand	Werkstoff	Norm
1	0.60 m	Rohr	50	3.91	P235GH	EN 10216-2
2	9.68 m	Rohr	80	5.49	P235GH	EN 10216-2
3	1 St	Anschweissstutzen	50	3.91	P235GH	MSS SP-97
4	2 St	Armatur mit Flanschen	80		P235GH	EN 558
5	2 St	Bogen 45 Grad	80	5.49	P235GH	EN 10253-2
6	2 St	Bogen 90	80	5.49	P235GH	EN 10253-2

... 5 weitere Positionen - siehe Excel

Nahtliste

Naht	Art	DN	Ort	Wo
WF1	Rundnaht	80	Anschluss Anfang	Baustelle
WF2	Rundnaht	80	Rohr / Vorschweissflansch	Werkstatt
WF3	Flanschverbindung	80	Vorschweissflansch / Armatur mit Flanschen	Werkstatt
WF4	Flanschverbindung	80	Armatur mit Flanschen / Armatur mit Flansc...	Werkstatt
WF5	Flanschverbindung	80	Armatur mit Flanschen / Vorschweissflansch	Werkstatt
WF6	Rundnaht	80	Vorschweissflansch / Rohr	Werkstatt
WF7	Rundnaht	80	Rohr / Bogen 90	Werkstatt
WF8	Rundnaht	80	Bogen 90 / Rohr	Werkstatt
WF9	Rundnaht	50	Anschweissstutzen auf DN 80	Werkstatt
WF10	Rundnaht	50	Abzweigrohr angeschweisst	Werkstatt

... 13 weitere Naehfte - siehe Excel

Halterungen



Halterung	Art	An Bauteil	Bei (mm)	Lage
FP1	Festpunkt	1	400	unten
GL1	Gleitlager	8	1200	unten
RS1	Rohrschelle	13	900	seitlich

Legende

- Werkstattnaht
- Baustellennaht
- Vorschweissflansch
- Armatur
- Fertig-T
- Anschweissstutzen
- Halterung, gefuellte = Festpunkt
- Positionsnummer aus der Stueckliste

PipeCraft - Rohrfolge

Zeichnung ISO-1001	Leitung 80-PL-1001-P235GH
Projekt / Anlage Testanlage Nord	NPD DN 80
Werkstoff P235GH	Schedule STD
Auslegungsdruck 16 bar	Auslegungstemperatur 120 Grad C
Isolierung 60 mm MW	Rohr gesamt 11.93 m
Naehfte / Flansche 19 / 4	Baustellennaehfte 3
Erstellt von T. Brors	Datum / Ansicht 04.09.2026 · Schweiessen

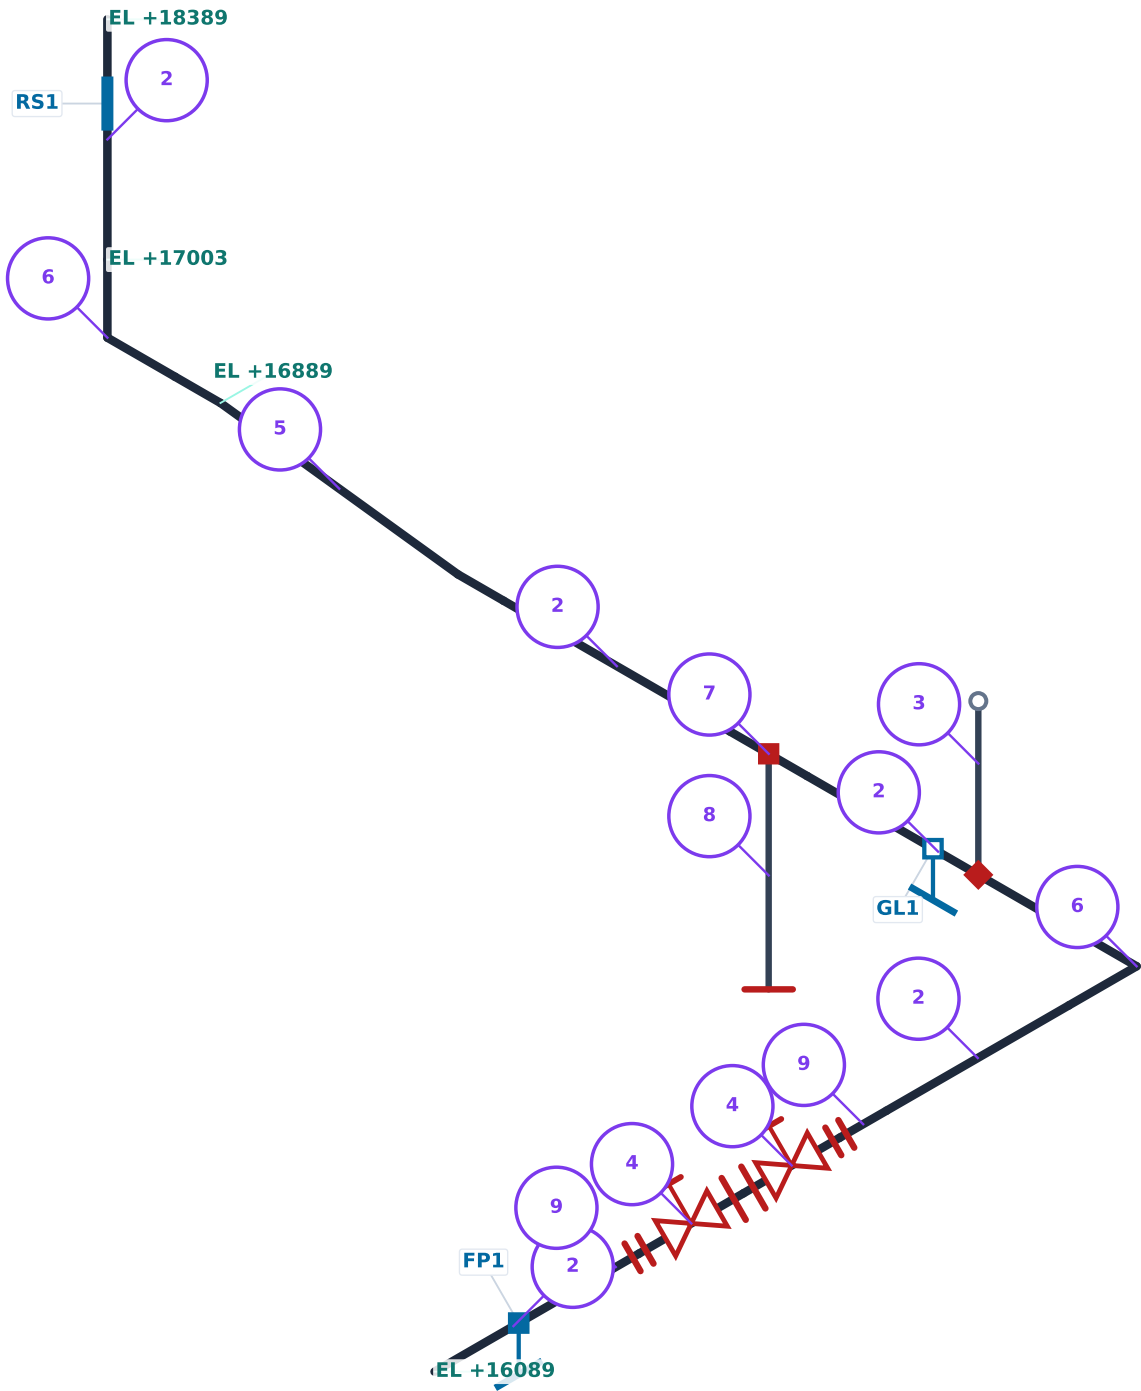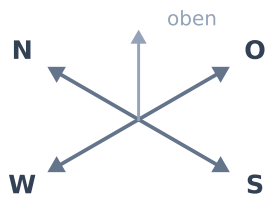

Stueckliste

Pos	Anzahl	Benennung	DN	Wand	Werkstoff	Norm
1	0.60 m	Rohr	50	3.91	P235GH	EN 10216-2
2	9.68 m	Rohr	80	5.49	P235GH	EN 10216-2
3	1 St	Anschweissstutzen	50	3.91	P235GH	MSS SP-97
4	2 St	Armatur mit Flanschen	80		P235GH	EN 558
5	2 St	Bogen 45 Grad	80	5.49	P235GH	EN 10253-2
6	2 St	Bogen 90	80	5.49	P235GH	EN 10253-2

... 5 weitere Positionen - siehe Excel

Nahtliste

Naht	Art	DN	Ort	Wo
WF1	Rundnaht	80	Anschluss Anfang	Baustelle
WF2	Rundnaht	80	Rohr / Vorschweissflansch	Werkstatt
WF3	Flanschverbindung	80	Vorschweissflansch / Armatur mit Flanschen	Werkstatt
WF4	Flanschverbindung	80	Armatur mit Flanschen / Armatur mit Flansc...	Werkstatt
WF5	Flanschverbindung	80	Armatur mit Flanschen / Vorschweissflansch	Werkstatt
WF6	Rundnaht	80	Vorschweissflansch / Rohr	Werkstatt
WF7	Rundnaht	80	Rohr / Bogen 90	Werkstatt
WF8	Rundnaht	80	Bogen 90 / Rohr	Werkstatt
WF9	Rundnaht	50	Anschweissstutzen auf DN 80	Werkstatt
WF10	Rundnaht	50	Abzweigrohr angeschweisst	Werkstatt

... 13 weitere Naehste - siehe Excel

Halterungen

Halterung	Art	An Bauteil	Bei (mm)	Lage
FP1	Festpunkt	1	400	unten
GL1	Gleitlager	8	1200	unten
RS1	Rohrschelle	13	900	seitlich

Legende

- Werkstattnaht
- ⊗ Baustellennaht
- | Vorschweissflansch
- ✕ Armatur
- Fertig-T
- ◆ Anschweissstutzen
- Halterung, gefuellte = Festpunkt
- Positionsnummer aus der Stueckliste

PipeCraft - Rohrfolge

Zeichnung ISO-1001	Leitung 80-PL-1001-P235GH
Projekt / Anlage Testanlage Nord	NPD DN 80
Werkstoff P235GH	Schedule STD
Auslegungsdruck 16 bar	Auslegungstemperatur 120 Grad C
Isolierung 60 mm MW	Rohr gesamt 11.93 m
Naehste / Flansche 19 / 4	Baustellennaehste 3
Erstellt von T. Brors	Datum / Ansicht 04.09.2026 · Montage